
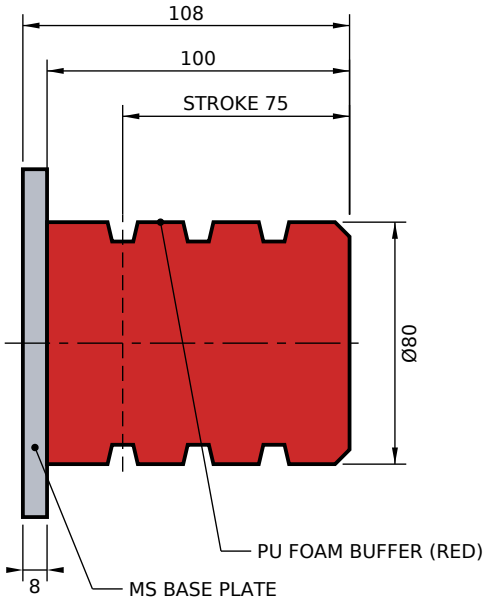



**PU BUFFER - BASE PLATE MOUNT**

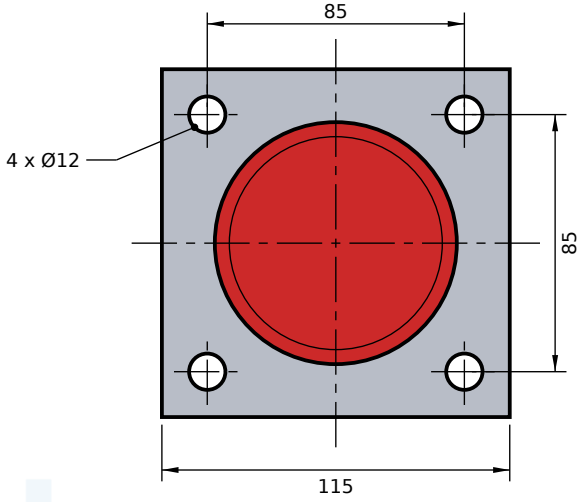


**VIEW FROM STRIKER END**

## Technical Parameters

| | | |
|---|---|---|
| Buffer diameter | Ø80 | mm |
| Buffer height | 100 | mm |
| Stroke (max. deflection) | 75 | mm |
| Energy capacity | 0.502 | kNm |
| Max. buffer force | 42 | kN |
| Base plate | 115 sq x 8 thk | mm |
| Mounting holes | 4 x Ø12 on 85 sq | mm |
| Buffer material | Polyurethane foam | |
| Base plate material | MS, painted | |

## NOTES

1. General arrangement for customer approval - not for manufacture.
2. Dashed line = striker face at maximum deflection.
3. Polyurethane (PU) foam buffer, shown in red, bonded to MS base plate; 4-bolt mounting.
4. Grooved profile controls the deflection characteristic; groove pattern per Adoni Tech design.
5. Operating temperature -20 to +80 °C.
6. Selection: www.cranebuffer.com | impactcal.netlify.app

adoniTech

| | | | |
|---|---|---|---|
| UNLESS OTHERWISE SPECIFIED:<br>DIMENSIONS ARE IN MILLIMETERS<br>GENERAL ARRANGEMENT - OUTLINE ONLY<br>DIMENSIONS SUBJECT TO CHANGE WITHOUT PRIOR NOTICE<br>PROJECTION: FIRST ANGLE | FINISH:<br>PU red / plate painted | DEBUR AND BREAK SHARP EDGES | DO NOT SCALE DRAWING / REVISION A |

| | NAME | SIGNATURE | DATE |
|---|---|---|---|
| DRAWN | PARESH ADAVANI | | 22-08-22 |
| CHK'D | | | |
| APPV'D | PARESH ADAVANI | | 24-08-22 |
| MFG | | | |
| Q.A | | | |

MATERIAL: PU foam, MS base plate | WEIGHT:

**ADONI TECH**
Addl. MIDC, Kodoli, Satara 415004
www.adonitech.co.in

TITLE:

**JHQ-C-3**

POLYURETHANE FOAM CRANE BUFFER - GA

DWG NO. **AT/GA/JHQC/3** | **A4**

SCALE: 1:2.5 | SHEET 1 OF 1