
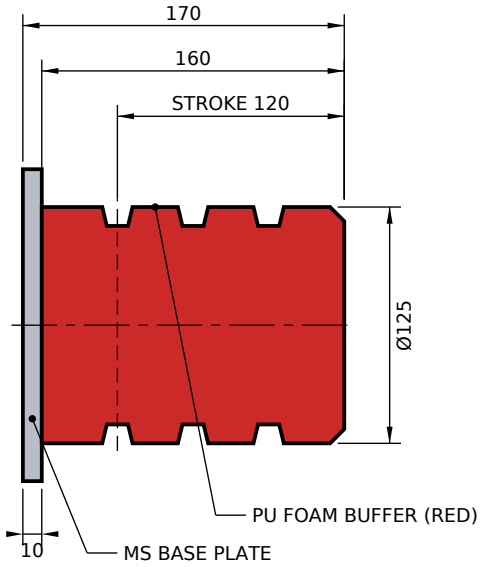


PU BUFFER - BASE PLATE MOUNT

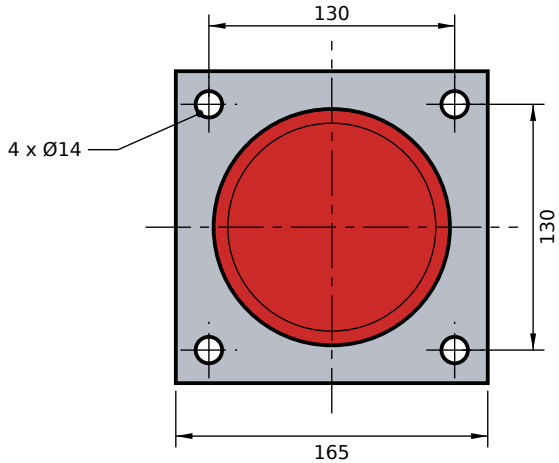

VIEW FROM STRIKER END

Technical Parameters

Buffer diameter	Ø125	mm
Buffer height	160	mm
Stroke (max. deflection)	120	mm
Energy capacity	1.96	kNm
Max. buffer force	103	kN
Base plate	165 sq x 10 thk	mm
Mounting holes	4 x Ø14 on 130 sq	mm
Buffer material	Polyurethane foam	
Base plate material	MS, painted	

NOTES

1. General arrangement for customer approval - not for manufacture.
2. Dashed line = striker face at maximum deflection.
3. Polyurethane (PU) foam buffer, shown in red, bonded to MS base plate; 4-bolt mounting.
4. Grooved profile controls the deflection characteristic; groove pattern per Adoni Tech design.
5. Operating temperature -20 to +80 °C.
6. Selection: www.cranebuffer.com | impactcal.netlify.app

adoniTech

UNLESS OTHERWISE SPECIFIED: DIMENSIONS ARE IN MILLIMETERS GENERAL ARRANGEMENT - OUTLINE ONLY DIMENSIONS SUBJECT TO CHANGE WITHOUT PRIOR NOTICE PROJECTION: FIRST ANGLE	FINISH: PU red / plate painted	DEBUR AND BREAK SHARP EDGES	DO NOT SCALE DRAWING / REVISION A

	NAME	SIGNATURE	DATE
DRAWN	PARESH ADAVANI		03-09-22
CHK'D			
APPV'D	PARESH ADAVANI		05-09-22
MFG			
Q.A			

MATERIAL: PU foam, MS base plate | WEIGHT:

ADONI TECH
Addl. MIDC, Kodoli, Satara 415004
www.adonitech.co.in

TITLE:

JHQ-C-9

POLYURETHANE FOAM CRANE BUFFER - GA

DWG NO. **AT/GA/JHQC/9** | **A4**

SCALE: 1:4 | SHEET 1 OF 1